


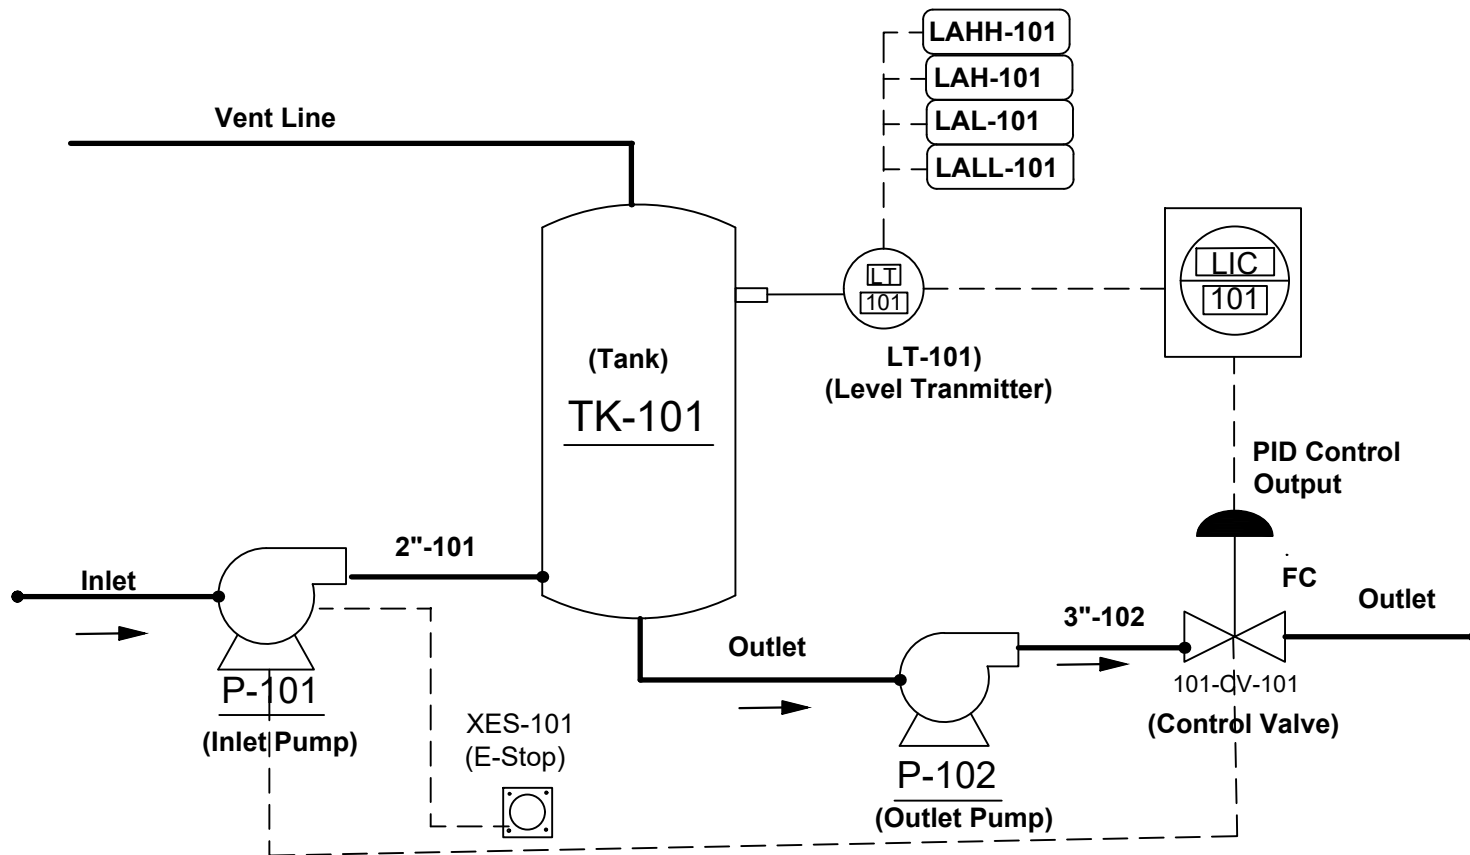

LEGEND		
	TK-101	Tank/Vessel
	P-101	Inlet Pump
	P-102	Outlet Pump
		Main Process Pipe Line
		Electrical Signal
		Flow Direction Arrow
	2"-101 3"-102	Line Identification
	LT-101	Level Transmitter
	LIC-101	Level Indicator Controller
	XES-101	Emergency Stop
		Flow Control Valve
	LAHH-101 LAH-101 LAL-101 LALL-101	Level Alarm High-High Level Alarm High Level Alarm Low Level Alarm Low-Low

TANK LEVEL CONTROL P&ID

Project: Tank Level Control

Engineer: Khazar Tarverdiyev

Date: 2026-09-07

Dwg. NO: P&ID-101